ORIGINAL

012

V-2201
SEPARATOR
SIZE: 762 mm O.D. x 2438mm S/S
D.P.: 9930 kPa @ 38°C

FE-2202
METER RUN
SIZE: 168.3mm -600#
MODEL: DANIEL SENIOR

FE-2206
METER RUN
SIZE: 168.3mm -600#
MODEL: DANIEL SENIOR

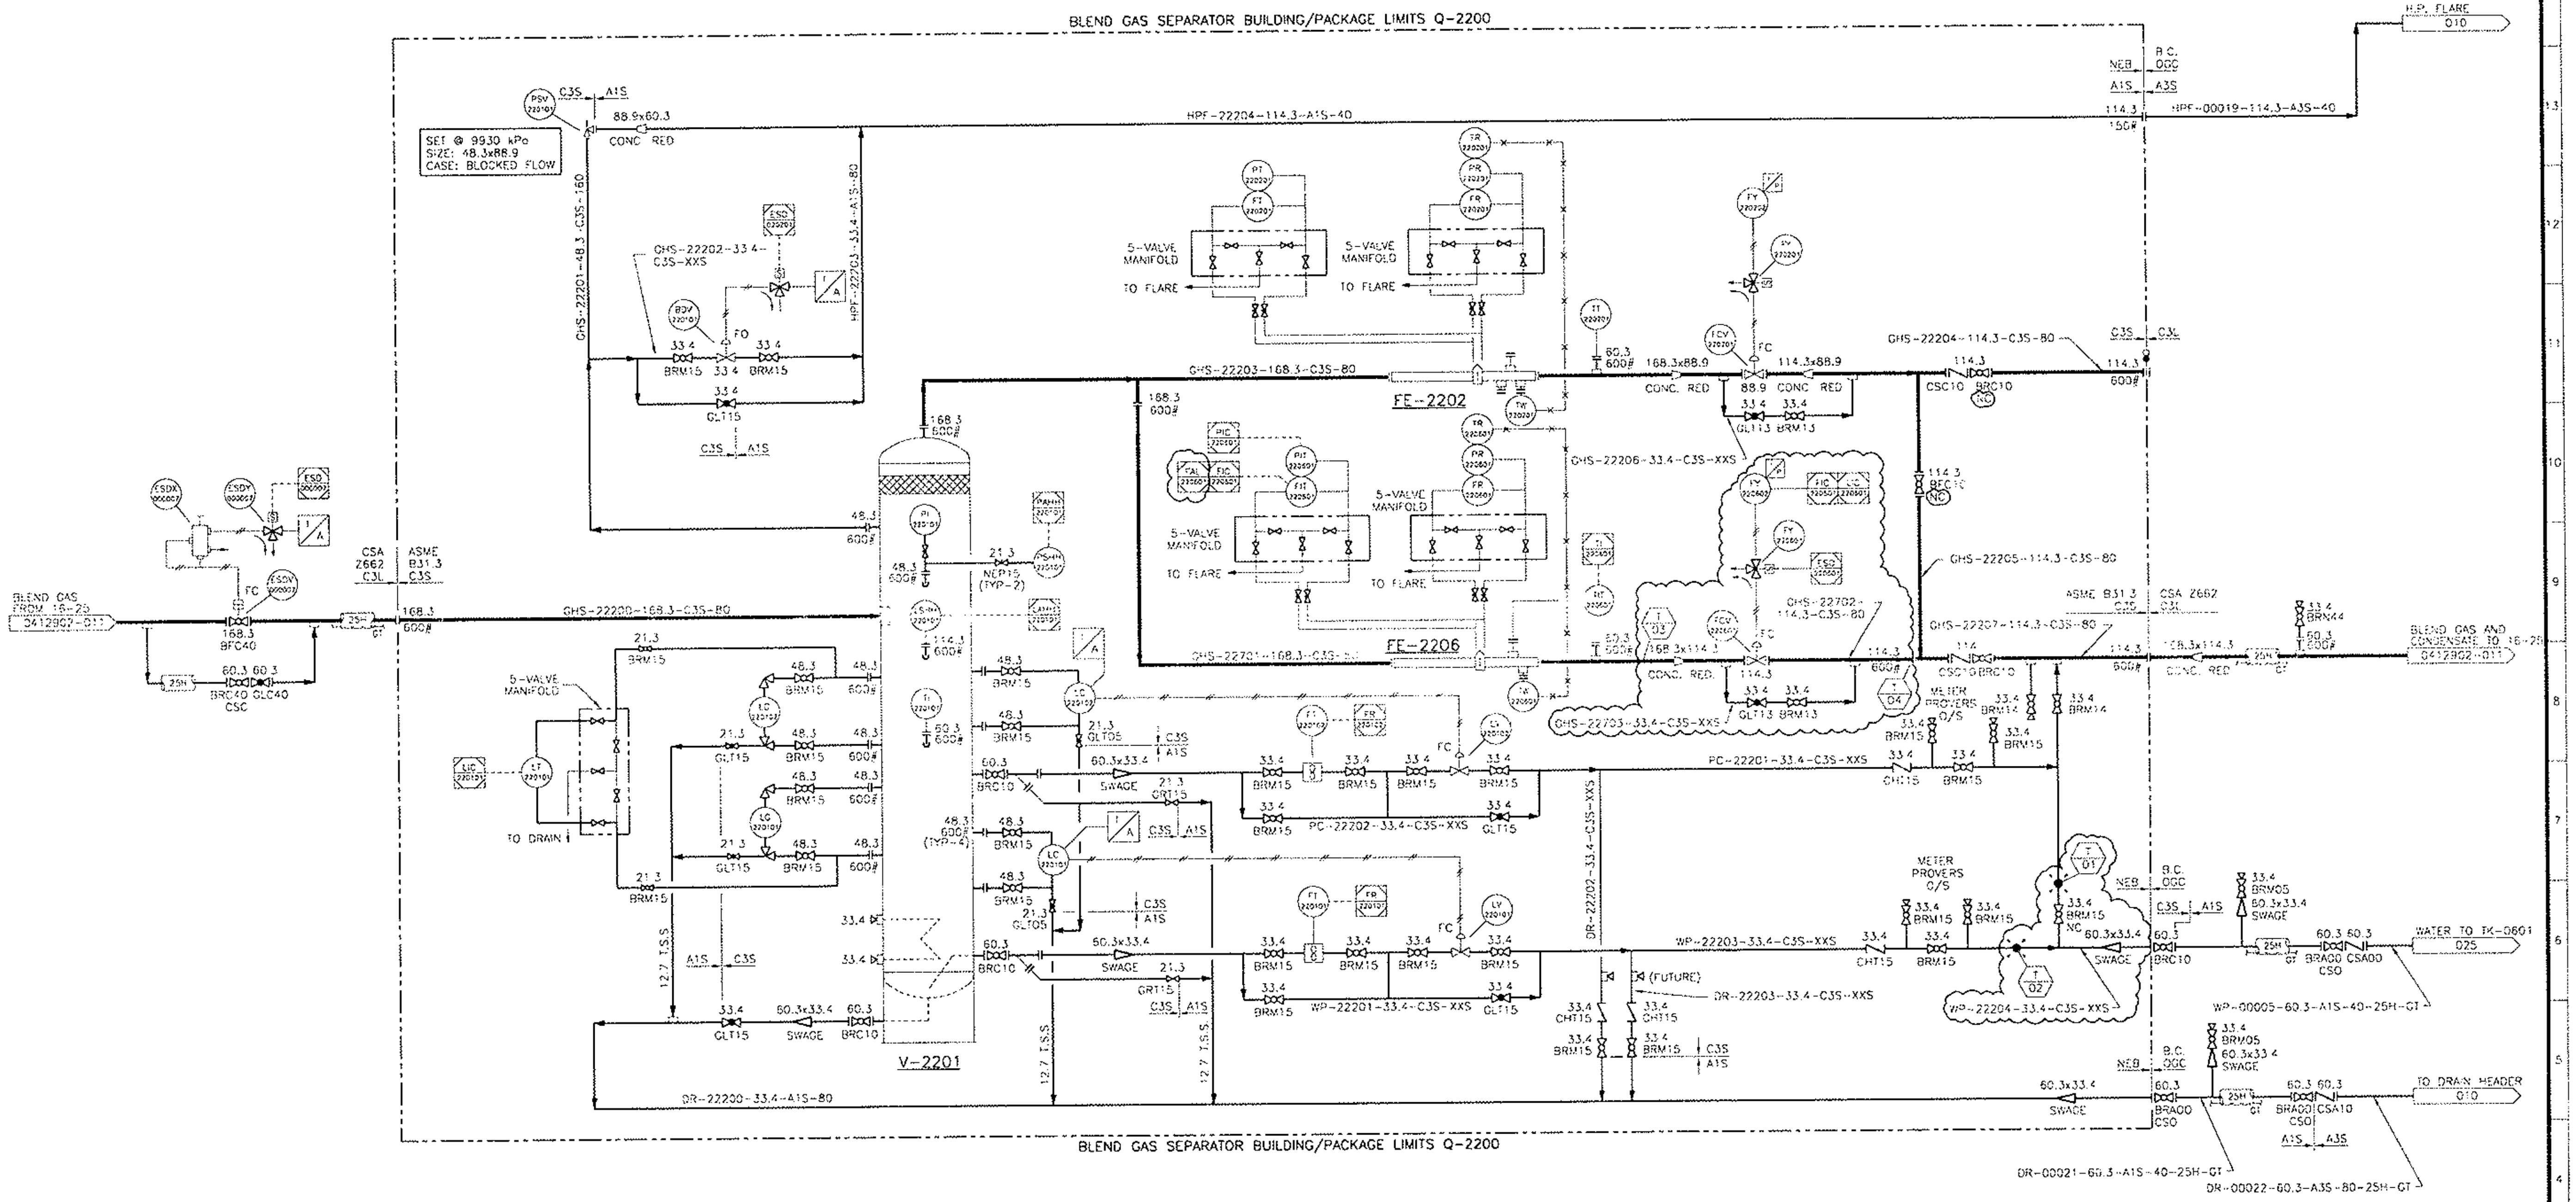

NOTES:
1. CLOUDED AREAS INDICATE NEW PIPING AND/OR EQUIPMENT ON SKID.

REVISION	DATE	REVISION DESCRIPTION	DRAWN/ DESIGN	DRAWING CHECK	DESIGN ENGINEER	DESIGN CHECK	WEI PROJECT APPROVAL
C	2007/02/26	RE-ISSUED FOR NEB APPROVAL #M0501 (EEL #041-29-00)	TC	Gmcolf			
B	2007/02/14	ISSUED FOR NEB APPROVAL #M0501 (EEL #041-29-02)	TC				
A	2007/02/08	ISSUED FOR INFORMATION #M0501 (EEL #041-29-00)	TC				

DRAWING NUMBER	REFERENCE DRAWING

NOTICE: THIS DRAWING HAS NOT BEEN PUBLISHED AND IS THE PROPERTY OF SPECTRA ENERGY MIDSTREAM CORP. AND IS LENT TO THE BORROWER FOR HIS CONFIDENTIAL USE ONLY, AND IN CONSIDERATION OF THE LOAN OF THIS DRAWING, THE BORROWER PROMISES AND AGREES THAT IT SHALL NOT BE REPRODUCED, COPIED, LENT OR OTHERWISE DISPOSED OF DIRECTLY OR INDIRECTLY, NOR USED FOR ANY PURPOSE OTHER THAN FOR WHICH IT IS FURNISHED.

EQUINOX
Engineering Ltd.

CLIENT: SPECTRA ENERGY MIDSTREAM CANADA PARTNER CORPORATION

PIPING AND INSTRUMENTATION DIAGRAM
BLEND GAS SEPARATOR PACKAGE
LSD 02-25-80-15 W6M

WEST DOE GAS PLANT

DRAWN/DESIGN	DESIGN ENGINEER	NETWORK ACTIVITY	SCALE	DATE
TC	NICOLE ABS	M0501	NTS	2007/02/08
DRAWING CHECK	**DESIGN CHECK**	**DRAWING NUMBER**		**REVISION**
G. TOMKINS	PAUL FOSS	030		C
WEI PROJECT APPROVAL				
SCOTT MCLEOD				